
PT. ROKINDO JAYA MANDIRI

Green Lake City, Rukan Fresh Market Blok B No.12 & 18
Cipondoh, Tangerang Tel: 021-5503476
rokindojayamandiri@rokindojayamandiri.com
www.rokindojayamandiri.com

Company / Customer	:	PT. DSV SOLUTIONS INDONESIA
Project Description	:	WIRING CONTROL PANEL
Drawing Number	:	
OC. Number	:	

MANUFACTURER (COMPANY)	:	PT. Rokindo Jaya Mandiri
CREATED ON	:	24/06/2026
DRAWING NUMBER	:	-

REV	REVISION	REV BY	DATE

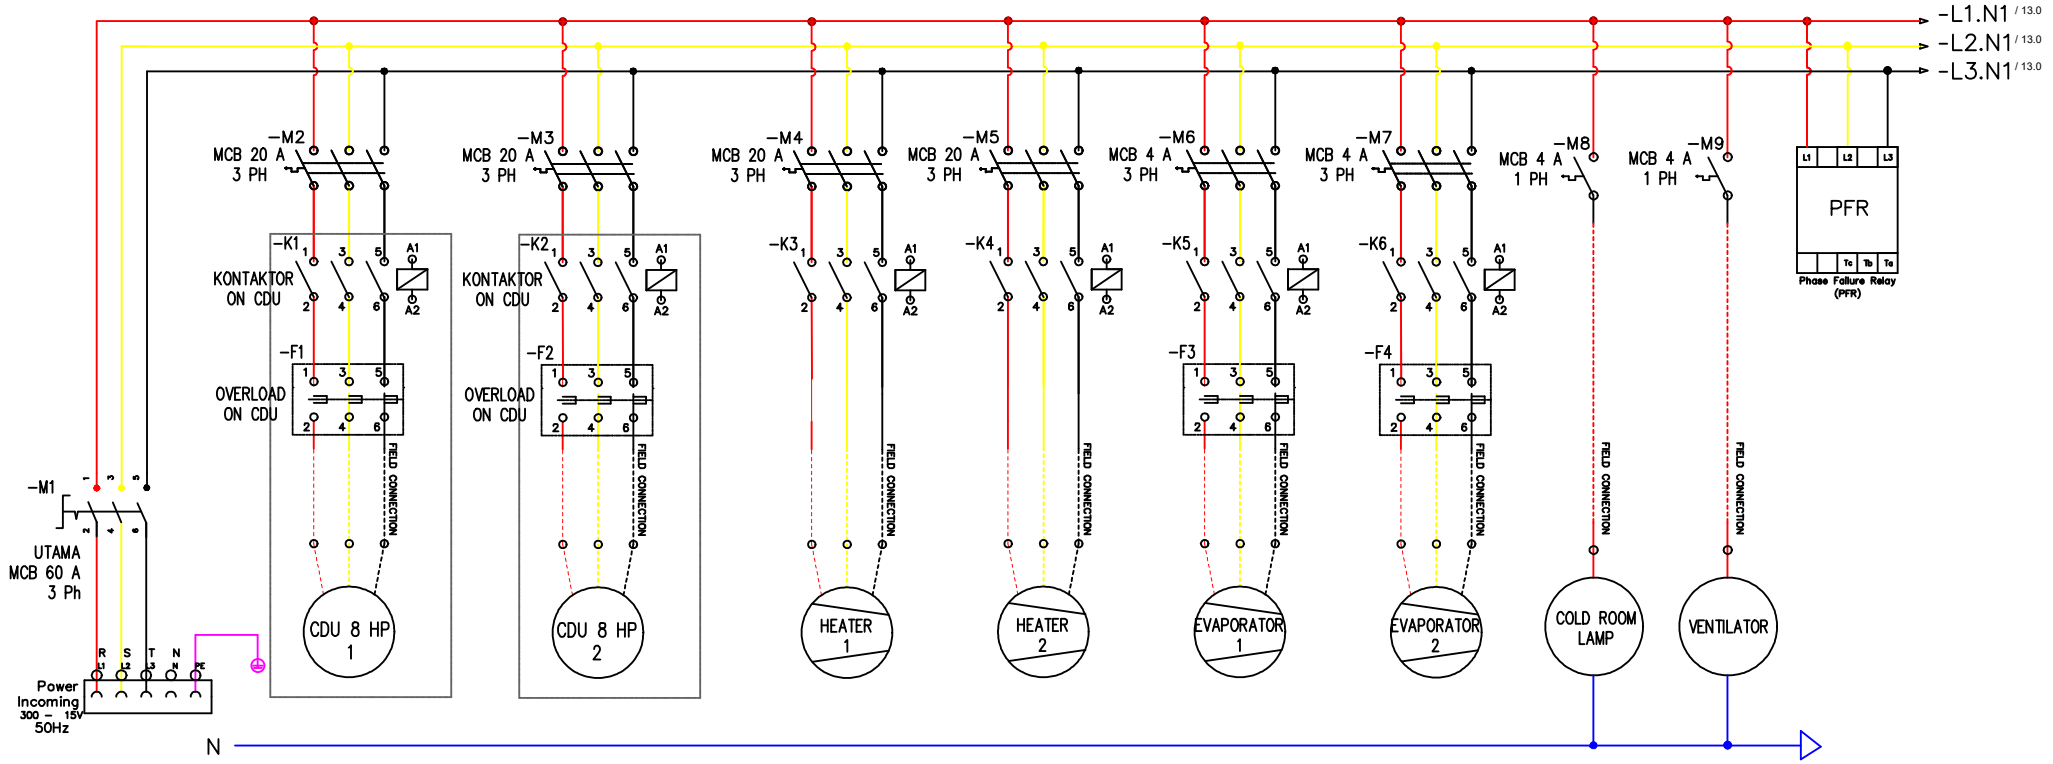


REV	DESCRIPTION	DATE	DRAWN	CHECKED	APPROVED
	FOR APPROVAL	24 - 06 - 2026	RY	RB	

RJM ROKINDO JAYA MANDIRI
Green Lake City, Rukan Fresh Market Blok B No.12 & 18
Cipondoh, Tangerang Tel: 021-5503476

PROJECT	PT. DSV SOLUTIONS INDONESIA	PANEL NAME	WIRING POWER
		DWG TITLE	WIRING DSV
LOKASI	Komp. Pergudangan WSK F1 - F20 Jl. Raya Bekasi KM.28,Medan Satria	DWG NO.	-

QUANTITY	1 UNIT
SCALE	NTS
SHEET NO.	02
TOTAL SHEET	04

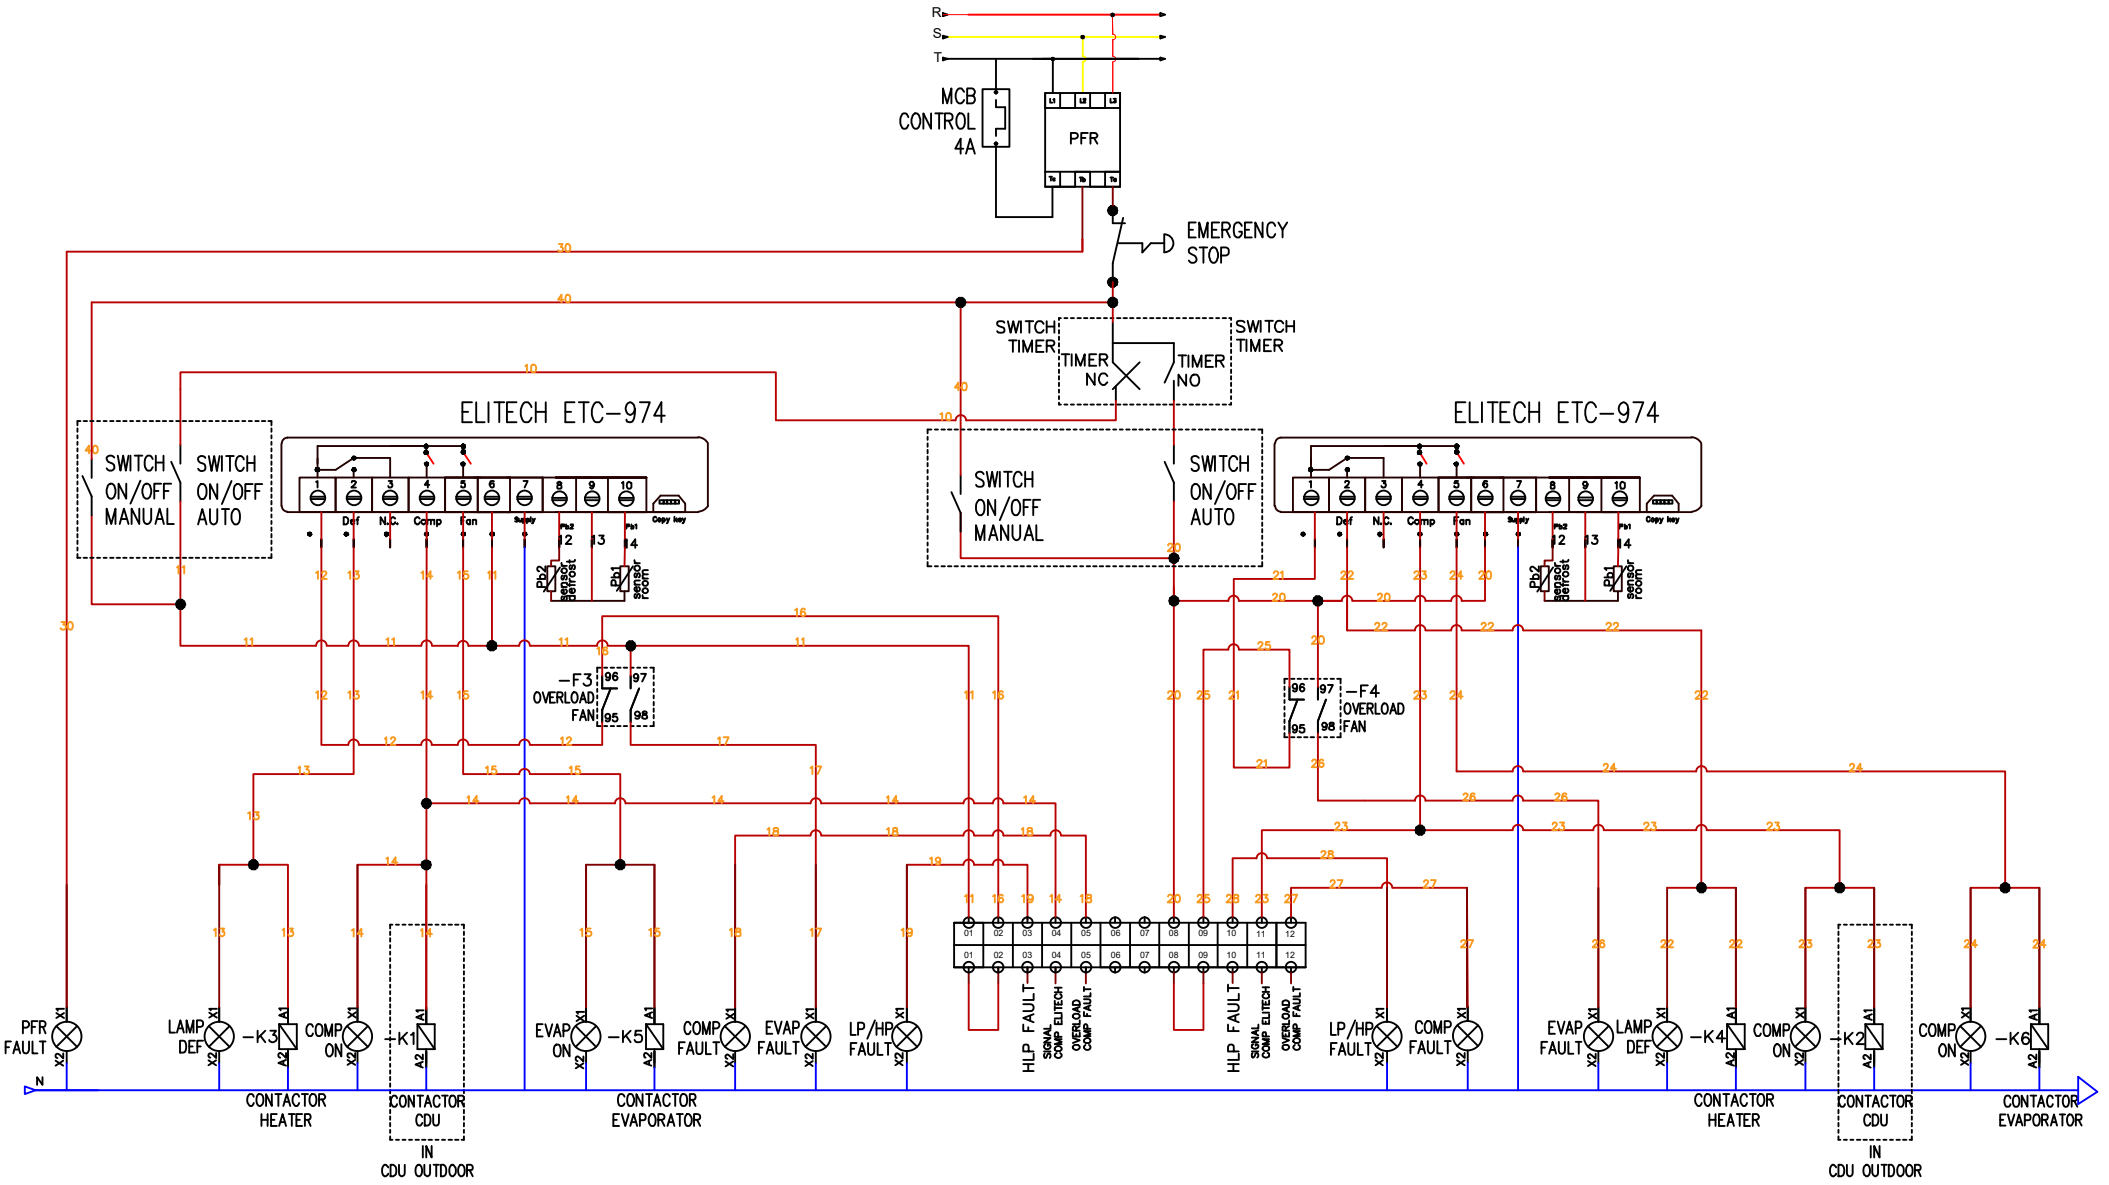



REV	DESCRIPTION	DATE	DRAWN	CHECKED	APPROVED
	FOR APPROVAL	24 - 06 - 2026	RY	RB	

RJM ROKINDO JAYA MANDIRI
Green Lake City, Rukan Fresh Market Blok B No.12 & 18
Cipondoh, Tangerang Tel: 021-5503476

PROJECT	PT. DSV SOLUTIONS INDONESIA	PANEL NAME	WIRING CONTROL
		DWG TITLE	WIRING DSV
LOKASI	Komp. Pergudangan WSK F1 - F20 Jl. Raya Bekasi KM.28,Medan Satria	DWG NO.	-

QUANTITY	1 UNIT
SCALE	NTS
SHEET NO.	03
TOTAL SHEET	04

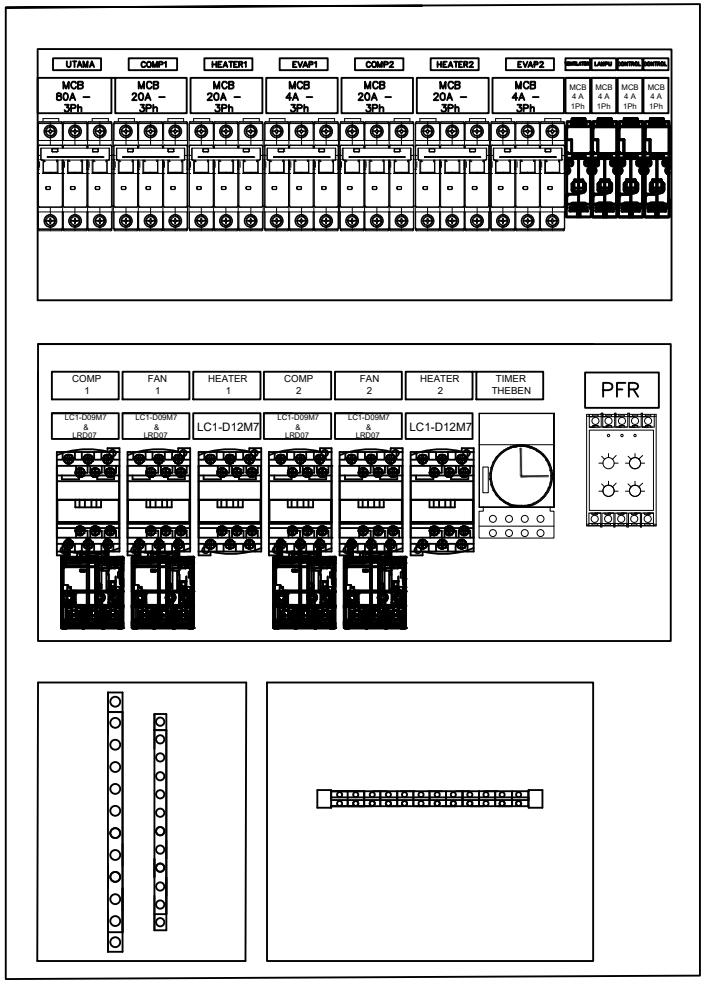

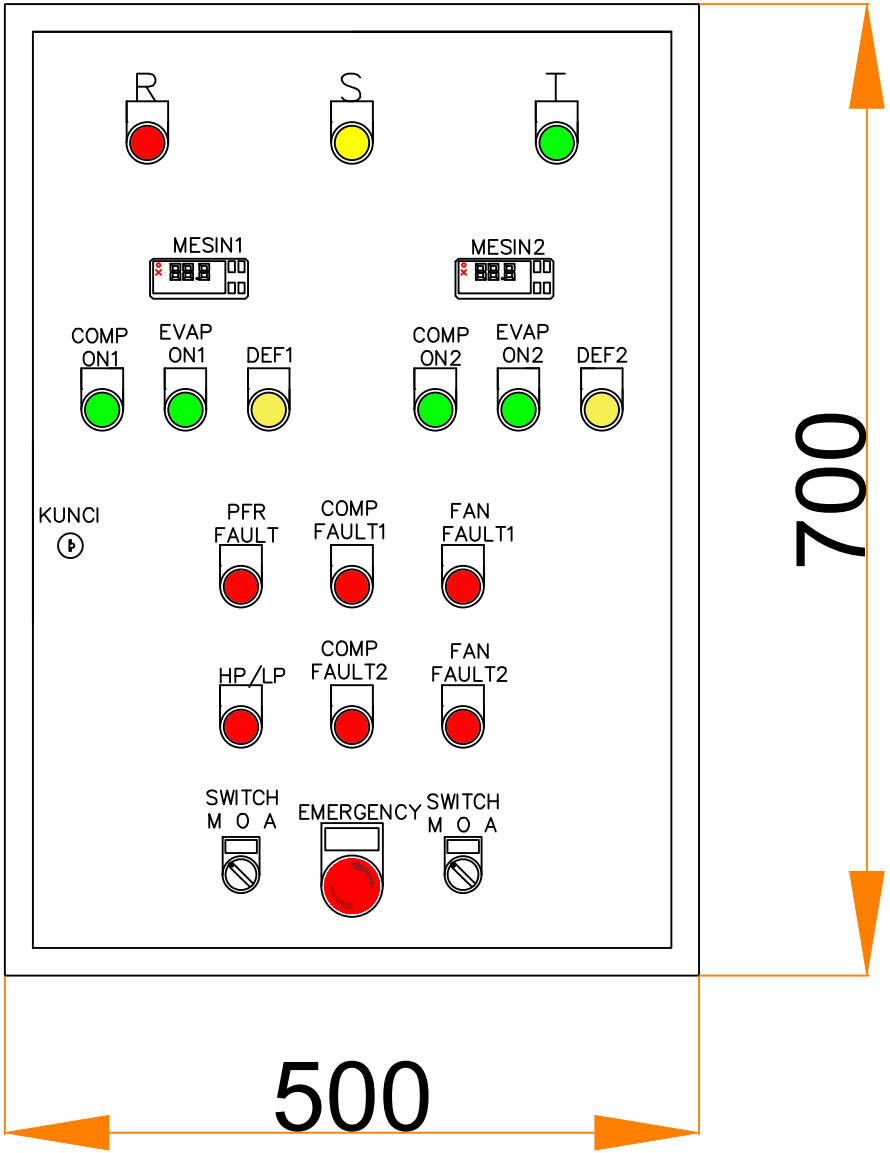

REV	DESCRIPTION	DATE	DRAWN	CHECKED	APPROVED
	FOR APPROVAL	24 - 06 - 2026	RY	RB	

RJM ROKINDO JAYA MANDIRI
Green Lake City, Rukan Fresh Market Blok B No.12 & 18
Cipondoh, Tangerang Tel: 021-5503476

PROJECT	PT. DSV SOLUTIONS INDONESIA	PANEL NAME	CONTROL PANEL
		DWG TITLE	WIRING DSV
LOKASI	Komp. Pergudangan WSK F1 - F20 Jl. Raya Bekasi KM.28,Medan Satria	DWG NO.	-

QUANTITY	1 UNIT
SCALE	NTS
SHEET NO.	04
TOTAL SHEET	04