
RJM | ROKINDO JAYA MANDIRI
Green Lake City, Rukan Fresh Market Blok B No.12 & 18
Cipondoh, Tangerang Tel: 021-5503476

Company / Customer	: LION SUPER INDO
Drawing Title	: SUB DISTRIBUTION PANEL
Drawing Number	: –
Location	: CITRA GARDEN SERPONG
Manufaturer (Company)	: PT ROKINDO JAYA MANDIRI
Date	: 15 – 09 – 2026

REV	REVISION	REV BY	DATE

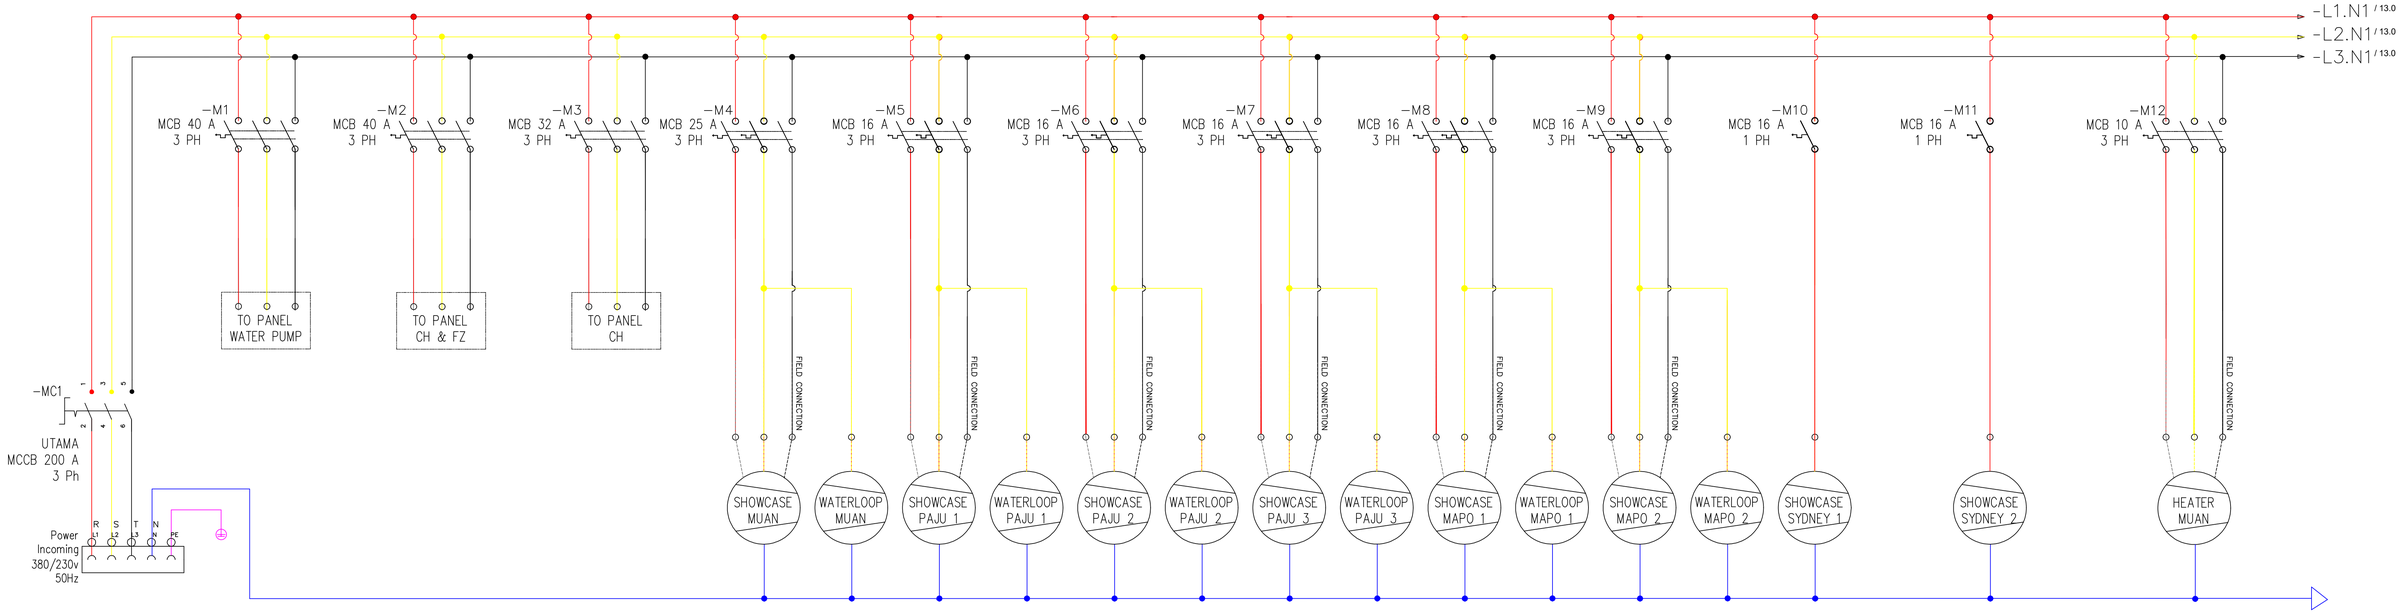



REV	DESCRIPTION	DATE	DRAWN	CHECKED	APPROVED
	FOR APPROVAL	15 - 09 - 2026	RY	RB	

RJM | ROKINDO JAYA MANDIRI
Green Lake City, Rukan Fresh Market Blok B No.12 & 18
Cipondoh, Tangerang Tel: 021-5503476

PROJECT	LION SUPER INDO	PANEL NAME	WIRING POWER
		DWG TITLE	SUB DISTRIBUTION PANEL
LOKASI	CITRA GARDEN SERPONG	DWG NO.	-

QUANTITY	-
SCALE	NTS
SHEET NO.	02
TOTAL SHEET	15

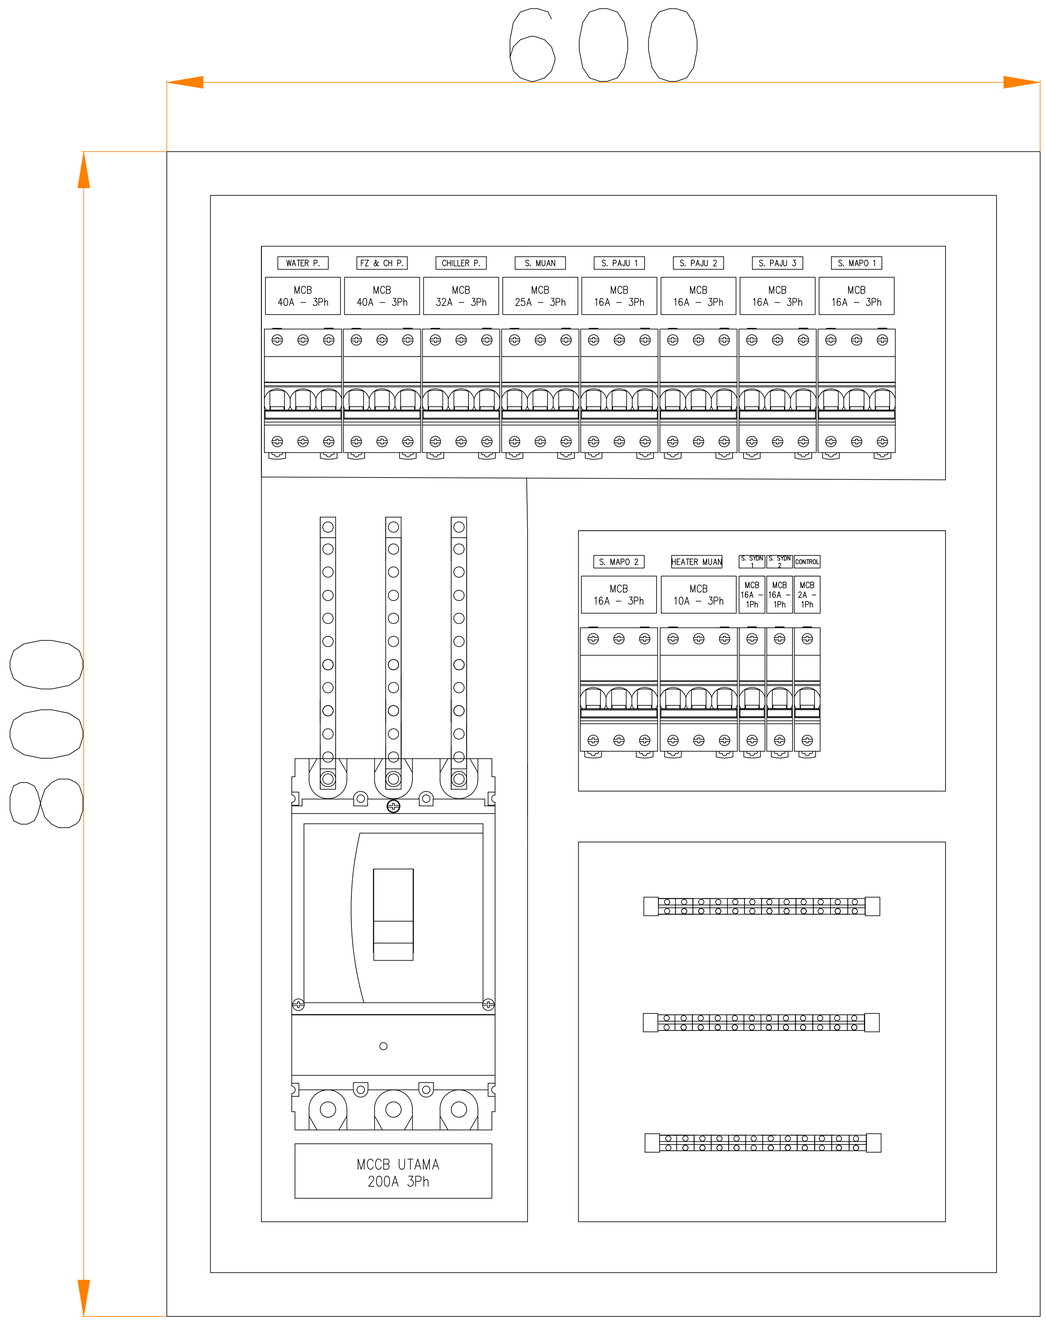

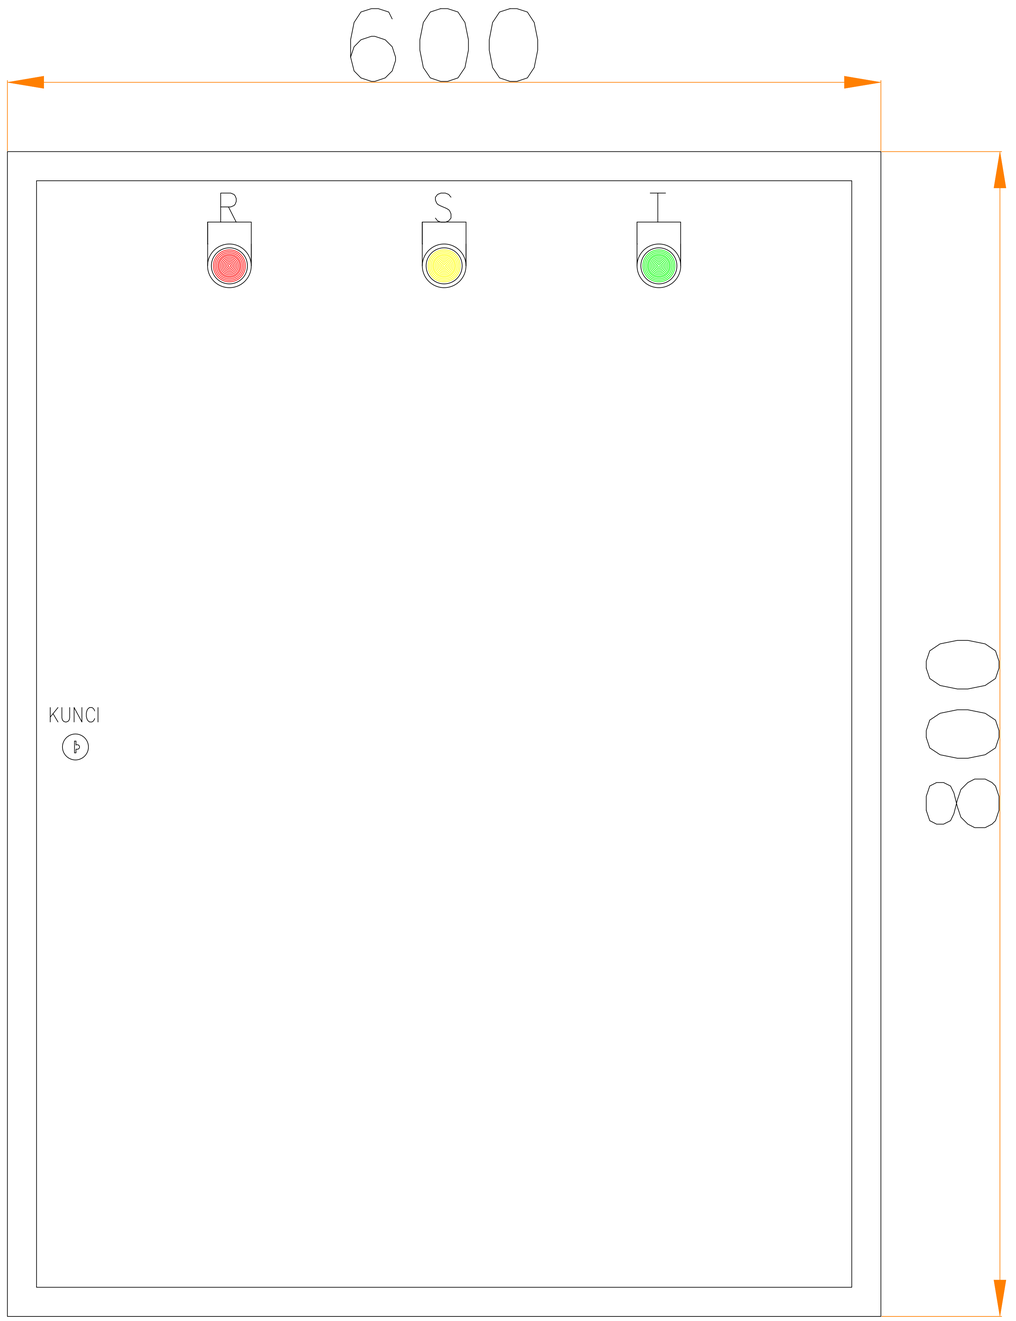

REV	DESCRIPTION	DATE	DRAWN	CHECKED	APPROVED
	FOR APPROVAL	15 - 09 - 2026	RY	RB	

ROKINDO JAYA MANDIRI
Green Lake City, Rukan Fresh Market Blok B No.12 & 18
Cipondoh, Tangerang Tel: 021-5503476


PROJECT	LION SUPER INDO	PANEL NAME	CONTROL PANEL
		DWG TITLE	SUB DISTRIBUTION PANEL
LOKASI	CITRA GARDEN SERPONG	DWG NO.	-

QUANTITY	-
SCALE	NTS
SHEET NO.	03
TOTAL SHEET	15

RJM | ROKINDO JAYA MANDIRI
Green Lake City, Rukan Fresh Market Blok B No.12 & 18
Cipondoh, Tangerang Tel: 021-5503476

Company / Customer	: LION SUPER INDO
Drawing Title	: WATER PUMP PANEL
Drawing Number	: –
Location	: CITRA GARDEN SERPONG
Manufaturer (Company)	: PT ROKINDO JAYA MANDIRI
Date	: 15 – 09 – 2026

REV	REVISION	REV BY	DATE

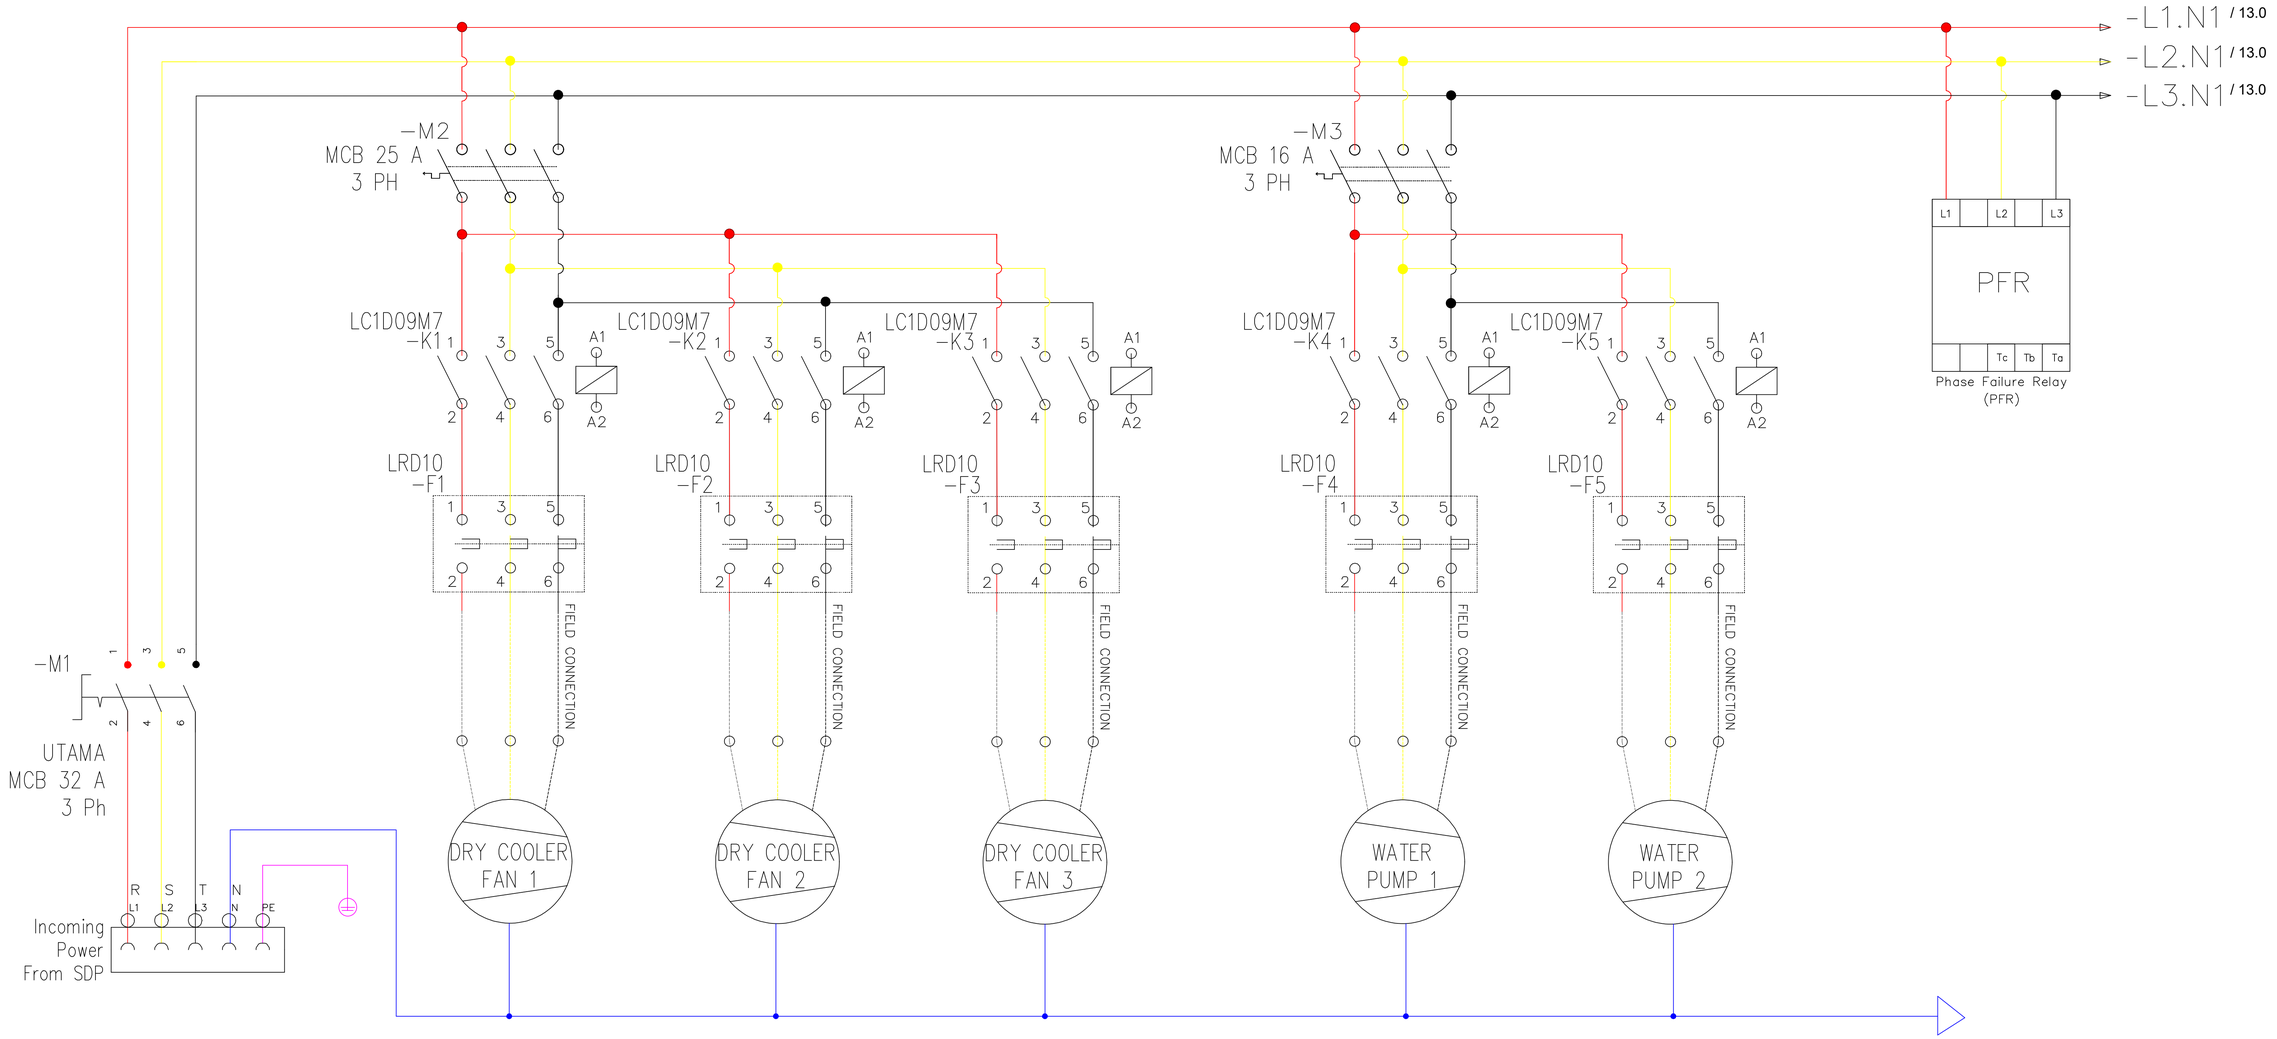


REV	DESCRIPTION	DATE	DRAWN	CHECKED	APPROVED
	FOR APPROVAL	15 - 09 - 2026	RY	RB	

RJM ROKINDO JAYA MANDIRI
Green Lake City, Rukan Fresh Market Blok B No.12 & 18
Cipondoh, Tangerang Tel: 021-5503476

PROJECT	LION SUPER INDO	PANEL NAME	WIRING POWER
		DWG TITLE	WATER PUMP PANEL
LOKASI	CITRA GARDEN SERPONG	DWG NO.	-

QUANTITY	-
SCALE	NTS
SHEET NO.	05
TOTAL SHEET	15

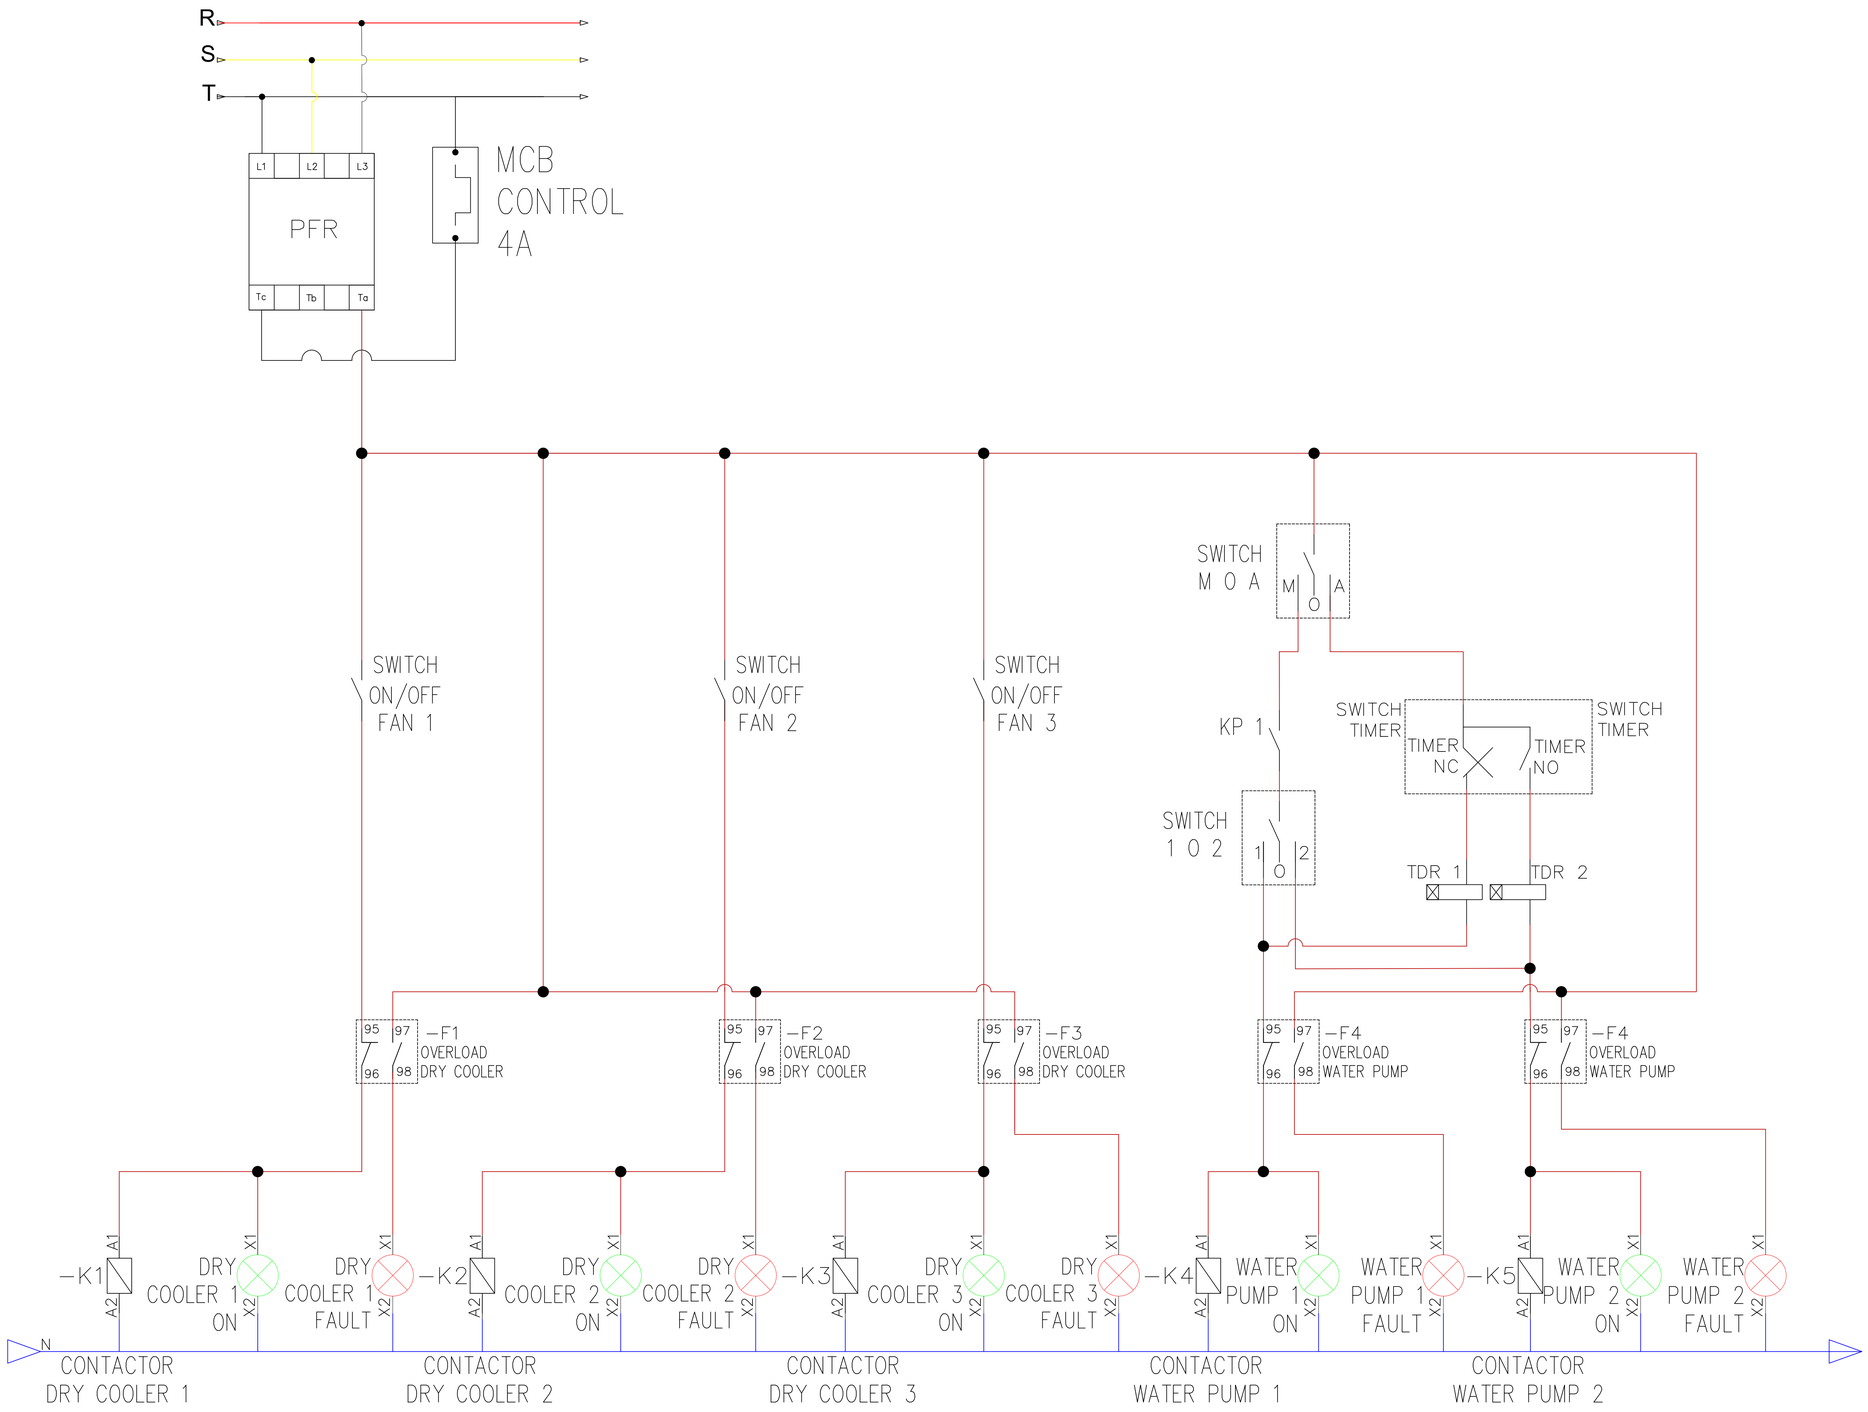



REV	DESCRIPTION	DATE	DRAWN	CHECKED	APPROVED
	FOR APPROVAL	15 - 09 - 2026	RY	RB	

RJM ROKINDO JAYA MANDIRI
Green Lake City, Rukan Fresh Market Blok B No.12 & 18
Cipondoh, Tangerang Tel: 021-5503476

PROJECT	LION SUPER INDO	PANEL NAME	WIRING CONTROL
		DWG TITLE	WATER PUMP PANEL
LOKASI	CITRA GARDEN SERPONG	DWG NO.	-

QUANTITY	-
SCALE	NTS
SHEET NO.	06
TOTAL SHEET	15

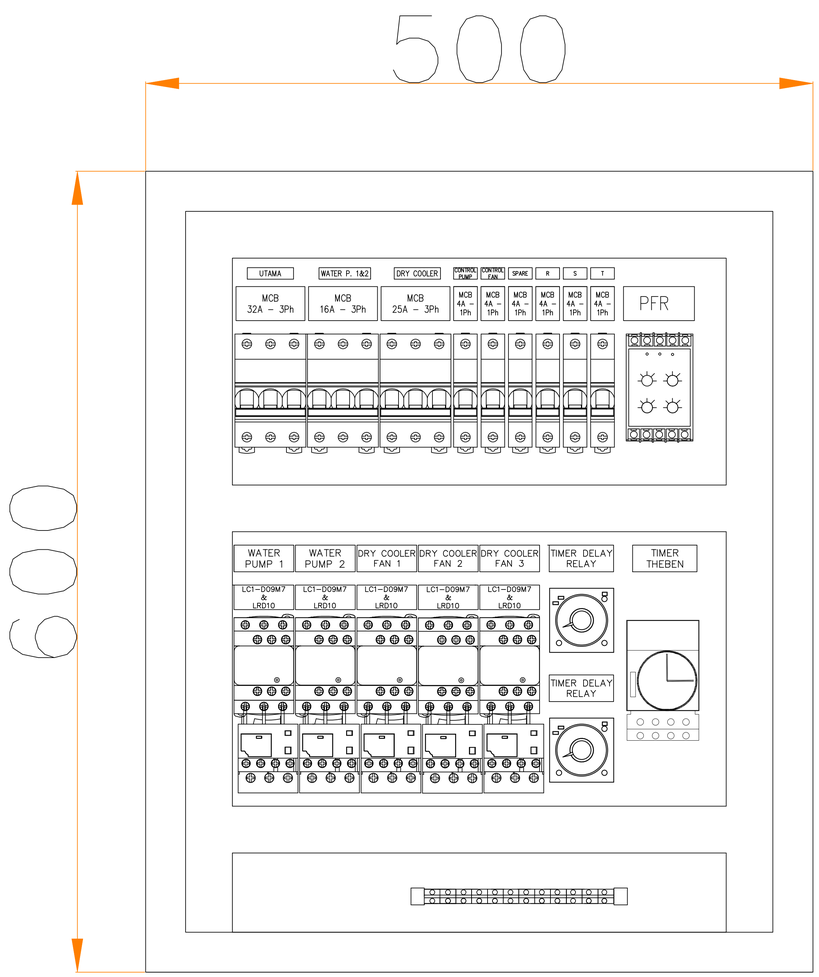

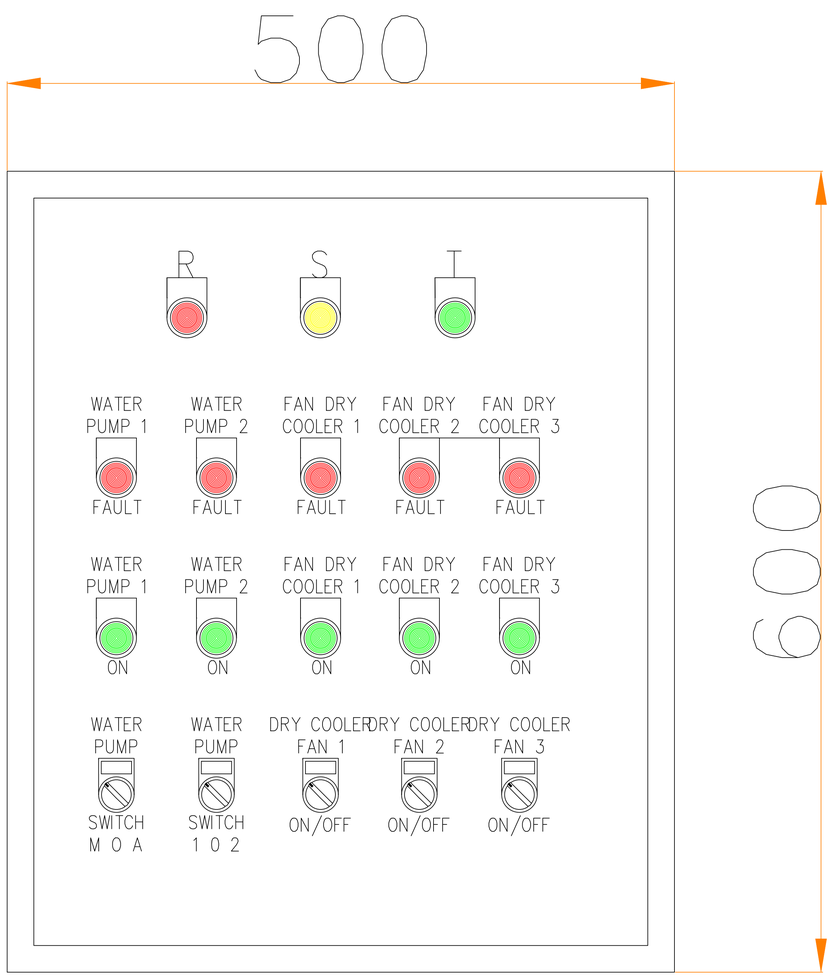

REV	DESCRIPTION	DATE	DRAWN	CHECKED	APPROVED
	FOR APPROVAL	15 - 09 - 2026	RY	RB	

RJM | ROKINDO JAYA MANDIRI
Green Lake City, Rukan Fresh Market Blok B No.12 & 18
Cipondoh, Tangerang Tel: 021-5503476


PROJECT	LION SUPER INDO	PANEL NAME	CONTROL PANEL
		DWG TITLE	WATER PUMP PANEL
LOKASI	CITRA GARDEN SERPONG	DWG NO.	-

QUANTITY	-
SCALE	NTS
SHEET NO.	07
TOTAL SHEET	15

RJM | ROKINDO JAYA MANDIRI
Green Lake City, Rukan Fresh Market Blok B No.12 & 18
Cipondoh, Tangerang Tel: 021-5503476

Company / Customer	: LION SUPER INDO
Drawing Title	: FREEZER & CHILLER PANEL
Drawing Number	: –
Location	: CITRA GARDEN SERPONG
Manufaturer (Company)	: PT ROKINDO JAYA MANDIRI
Date	: 15 – 09 – 2026

REV	REVISION	REV BY	DATE

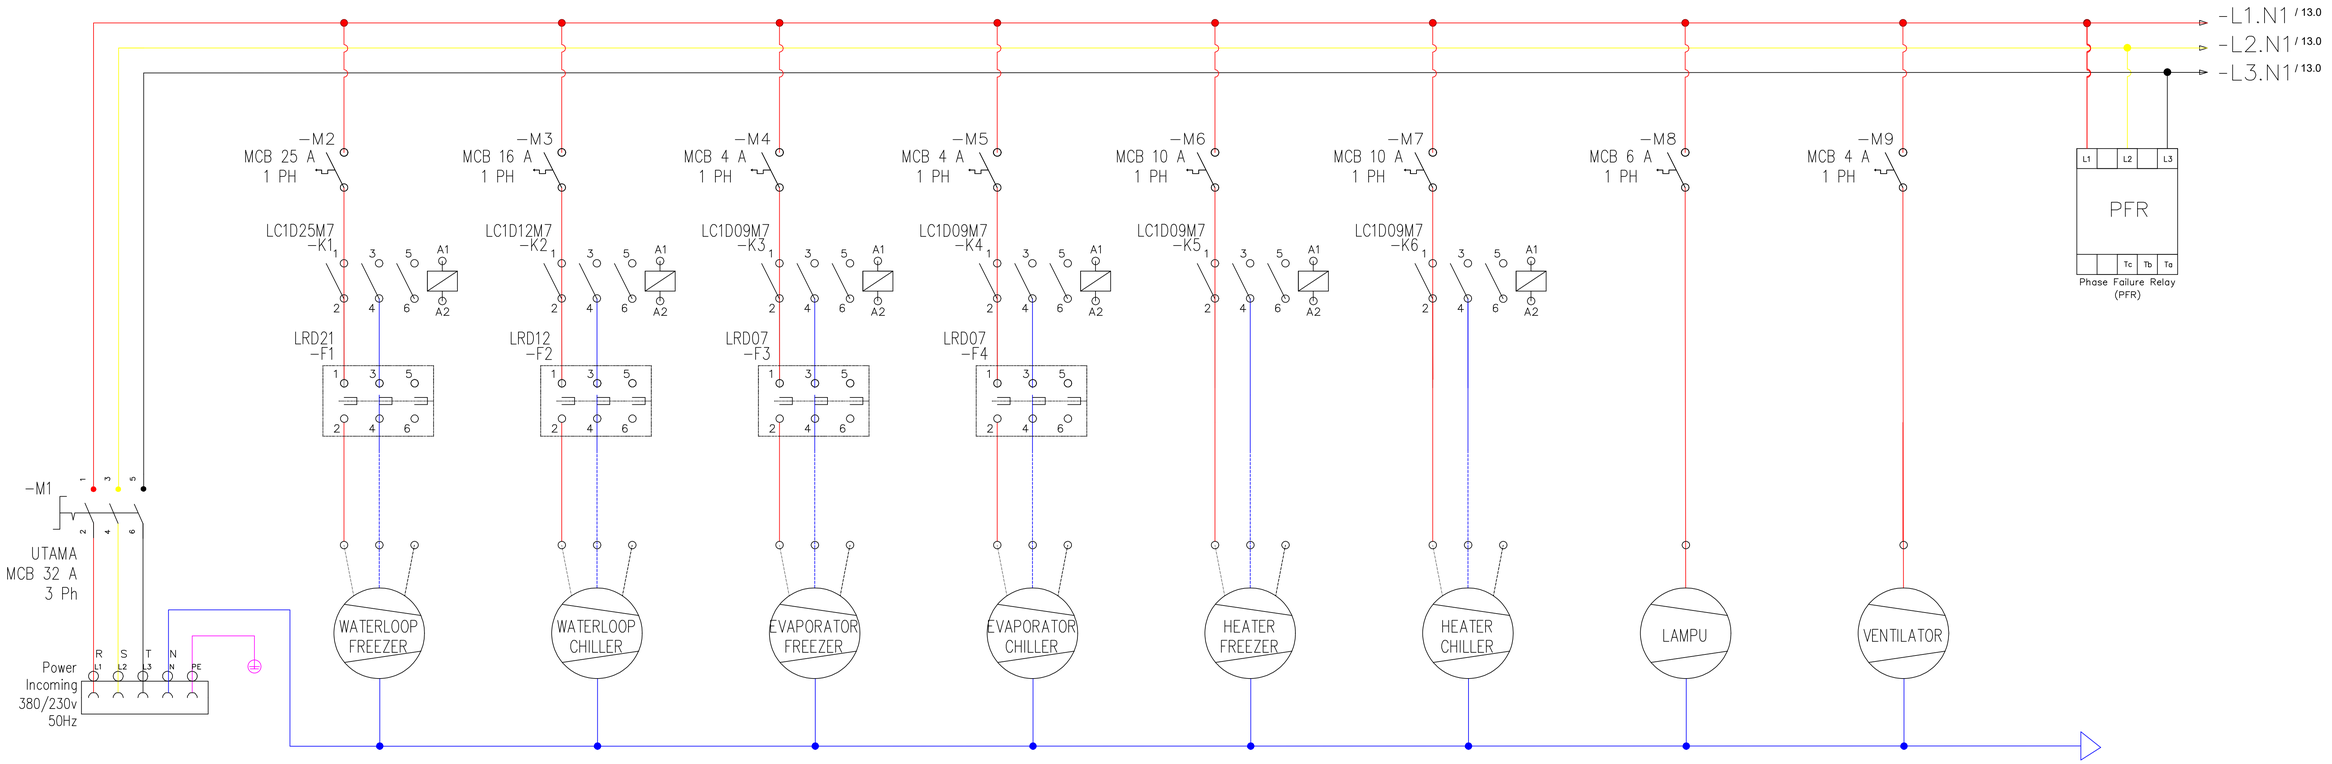


REV	DESCRIPTION	DATE	DRAWN	CHECKED	APPROVED
	FOR APPROVAL	15 - 09 - 2026	RY	RB	

RJM | ROKINDO JAYA MANDIRI
Green Lake City, Rukan Fresh Market Blok B No.12 & 18
Cipondoh, Tangerang Tel: 021-5503476

PROJECT	LION SUPER INDO	PANEL NAME	WIRING POWER
		DWG TITLE	FREEZER & CHILLER PANEL
LOKASI	CITRA GARDEN SERPONG	DWG NO.	-

QUANTITY	-
SCALE	NTS
SHEET NO.	09
TOTAL SHEET	15

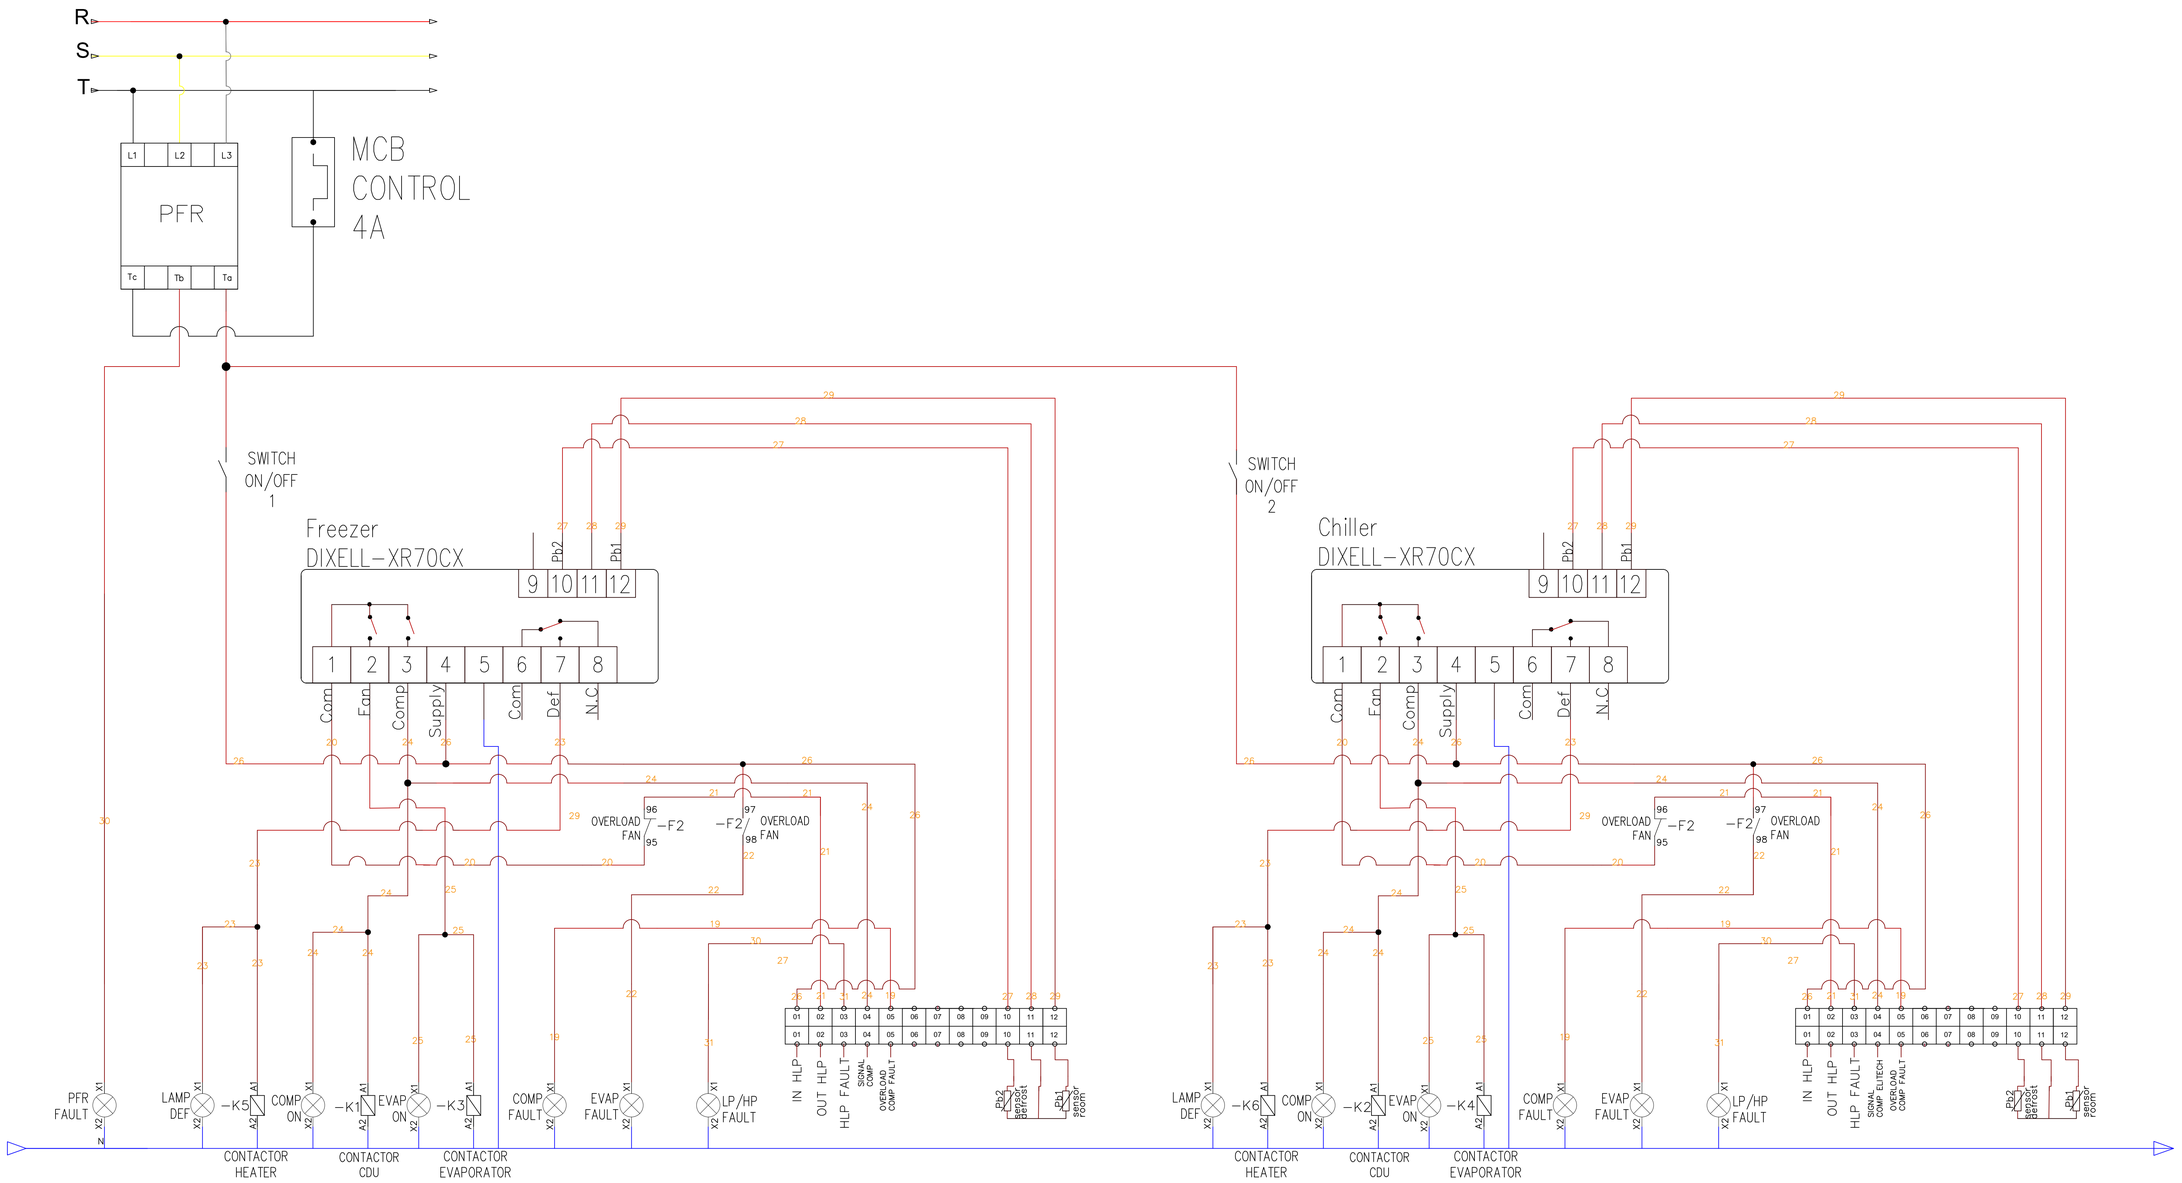

REV	DESCRIPTION	DATE	DRAWN	CHECKED	APPROVED
	FOR APPROVAL	15 - 09 - 2026	RY	RB	

RJM | ROKINDO JAYA MANDIRI
Green Lake City, Rukan Fresh Market Blok B No.12 & 18
Cipondoh, Tangerang Tel: 021-5503476

PROJECT	LION SUPER INDO	PANEL NAME	WIRING CONTROL
		DWG TITLE	FREEZER & CHILLER PANEL
LOKASI	CITRA GARDEN SERPONG	DWG NO.	-

QUANTITY	-
SCALE	NTS
SHEET NO.	10
TOTAL SHEET	15

500

500

UTAMA

CDU FZ	CDU CH	DEFF FZ	DEFF CH	FAN FZ	FAN CH	CONTROL	LAMPU	R	S	T
MCB 32A – 3Ph	MCB 25A – 1Ph	MCB 16A – 1Ph	MCB 10A – 1Ph	MCB 10A – 1Ph	MCB 4A – 1Ph	MCB 4A – 1Ph	MCB 4A – 1Ph	MCB 6A – 1Ph	MCB 4A – 1Ph	MCB 4A – 1Ph	MCB 4A – 1Ph

PFR

CDU FZ	CDU CH	FAN FZ	FAN CH	HEATER FZ	HEATER CH
LC1–D25M7 & LRD21	LC1–D12M7 & LRD12	LC1–D09M7	LC1–D09M7	LC1–D09M7	LC1–D09M7

R S T

FREEZER

CHILLER

COMP ON1 | EVAP ON1 | DEF1

COMP ON2 | EVAP ON2 | DEF2

KUNCI

HP/LP 1 | COMP FAULT1 | FAN FAULT1

HP/LP 2 | COMP FAULT2 | FAN FAULT2

ON/OFF | PFR FAULT | ON/OFF

REV	DESCRIPTION	DATE	DRAWN	CHECKED	APPROVED
	FOR APPROVAL	15 - 09 - 2026	RY	RB	


ROKINDO JAYA MANDIRI
Green Lake City, Rukan Fresh Market Blok B No.12 & 18
Cipondoh, Tangerang Tel: 021-5503476

PROJECT	LION SUPER INDO
LOKASI	CITRA GARDEN SERPONG
PANEL NAME	CONTROL PANEL
DWG TITLE	FREEZER & CHILLER PANEL
DWG NO.	-
QUANTITY	-
SCALE	NTS
SHEET NO.	11
TOTAL SHEET	15

RJM | ROKINDO JAYA MANDIRI
Green Lake City, Rukan Fresh Market Blok B No.12 & 18
Cipondoh, Tangerang Tel: 021-5503476

Company / Customer	: LION SUPER INDO
Drawing Title	: CHILLER PANEL
Drawing Number	: –
Location	: CITRA GARDEN SERPONG
Manufaturer (Company)	: PT ROKINDO JAYA MANDIRI
Date	: 15 – 09 – 2026

REV	REVISION	REV BY	DATE

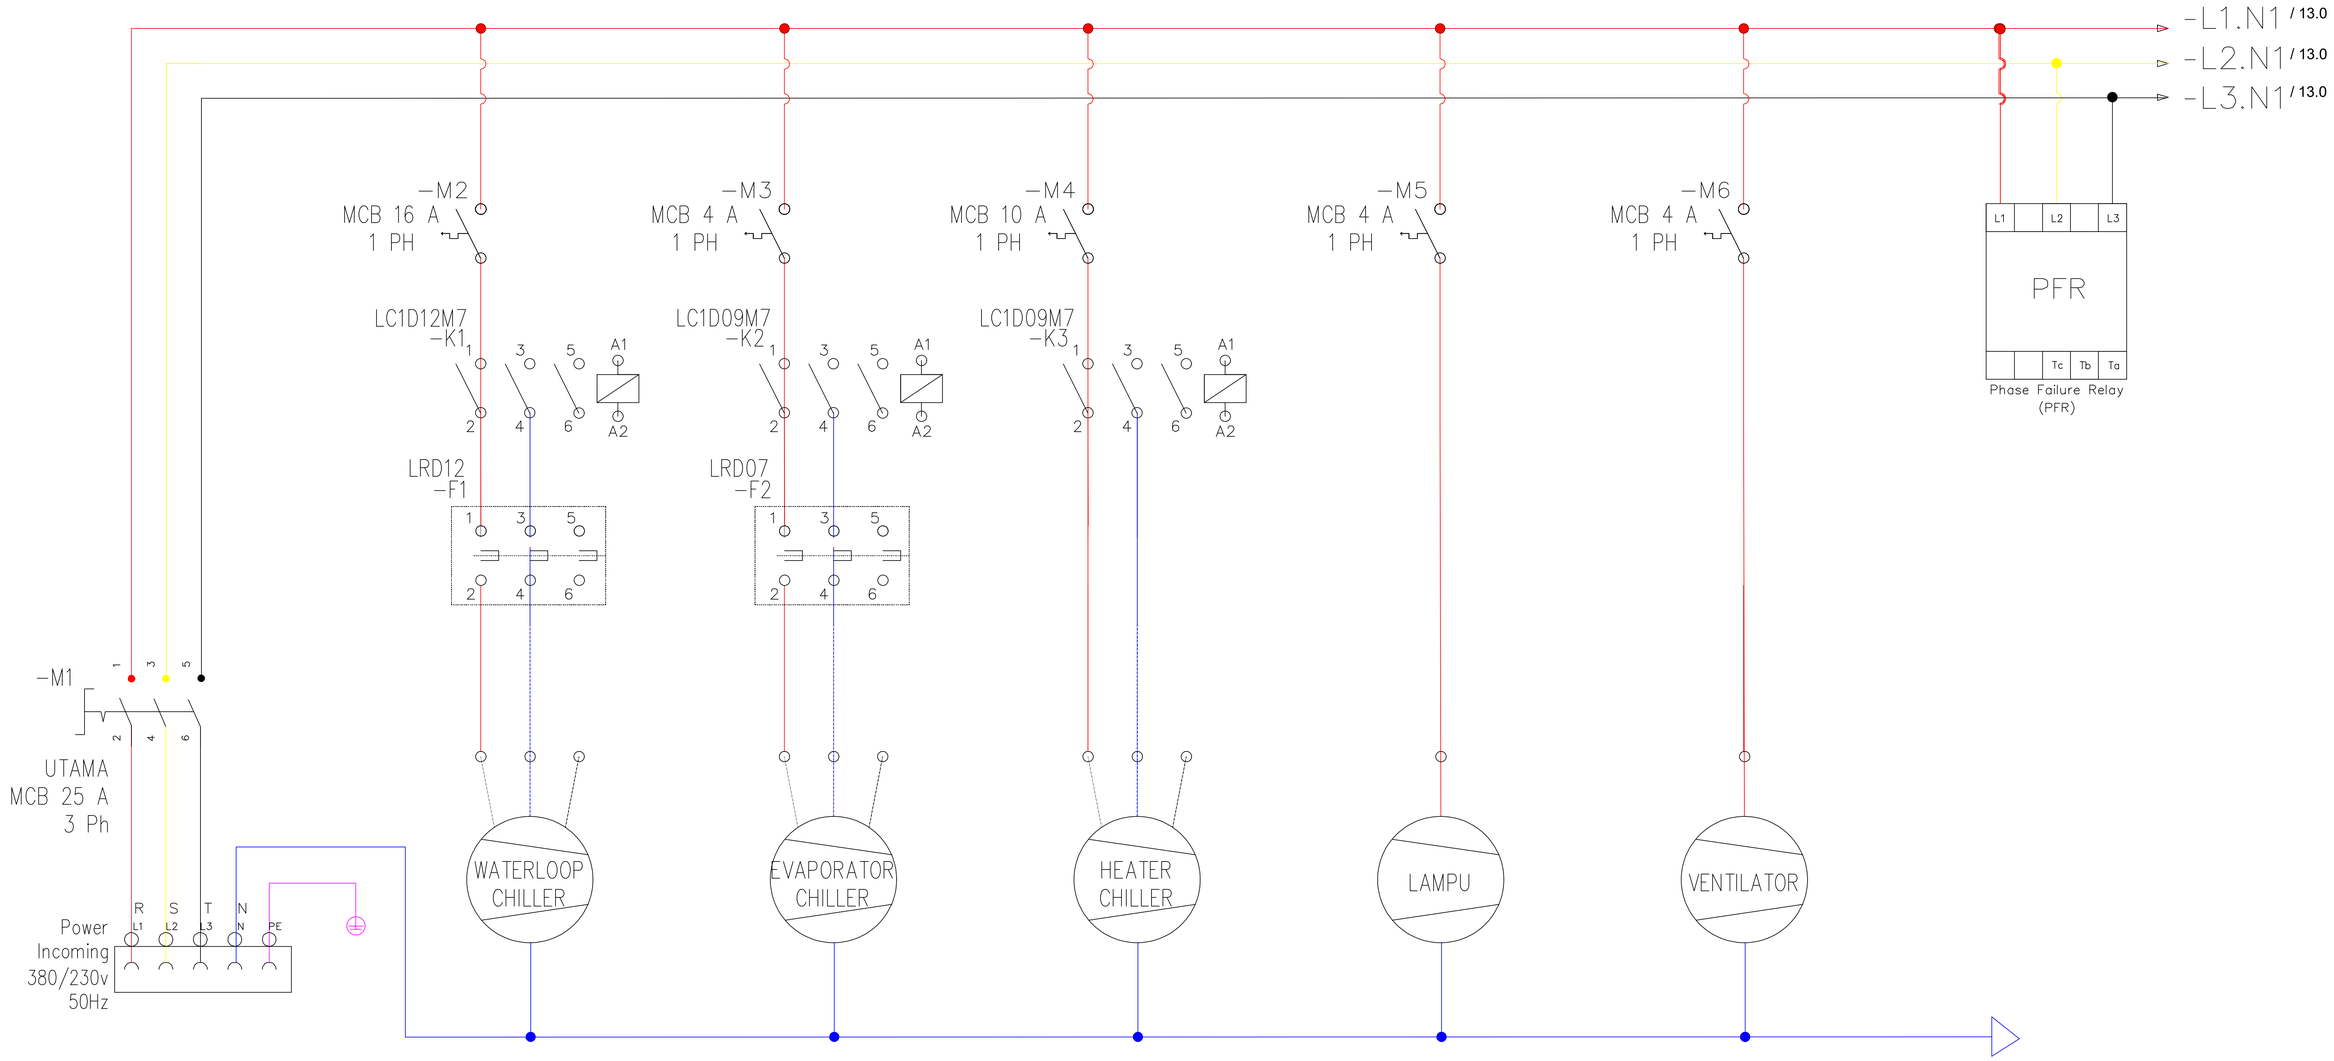


REV	DESCRIPTION	DATE	DRAWN	CHECKED	APPROVED
	FOR APPROVAL	15 - 09 - 2026	RY	RB	

ROKINDO JAYA MANDIRI
Green Lake City, Rukan Fresh Market Blok B No.12 & 18
Cipondoh, Tangerang Tel: 021-5503476

PROJECT	LION SUPER INDO	PANEL NAME	WIRING POWER
		DWG TITLE	CHILLER PANEL
LOKASI	CITRA GARDEN SERPONG	DWG NO.	-

QUANTITY	-
SCALE	NTS
SHEET NO.	13
TOTAL SHEET	15

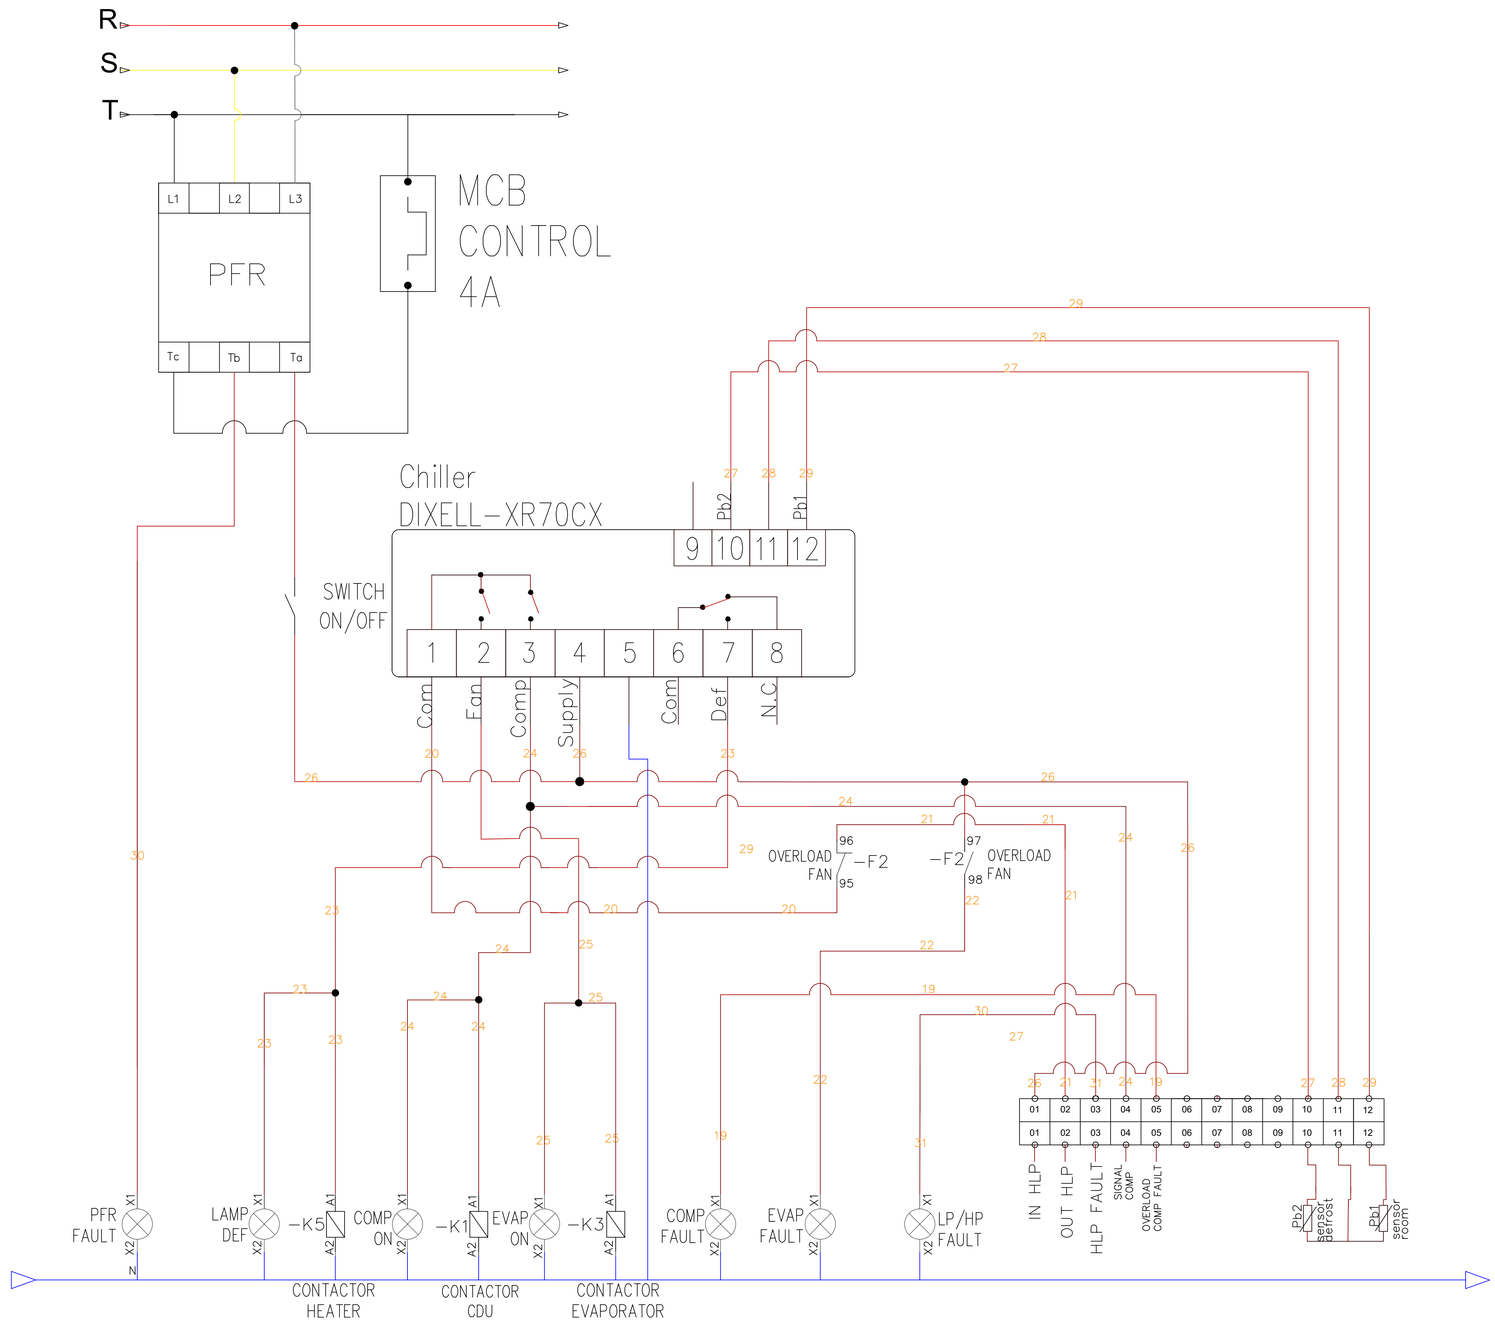



REV	DESCRIPTION	DATE	DRAWN	CHECKED	APPROVED
	FOR APPROVAL	15 - 09 - 2026	RY	RB	

RJM ROKINDO JAYA MANDIRI
Green Lake City, Rukan Fresh Market Blok B No.12 & 18
Cipondoh, Tangerang Tel: 021-5503476

PROJECT	LION SUPER INDO	PANEL NAME	WIRING CONTROL
		DWG TITLE	CHILLER PANEL
LOKASI	CITRA GARDEN SERPONG	DWG NO.	-

QUANTITY	-
SCALE	NTS
SHEET NO.	14
TOTAL SHEET	15

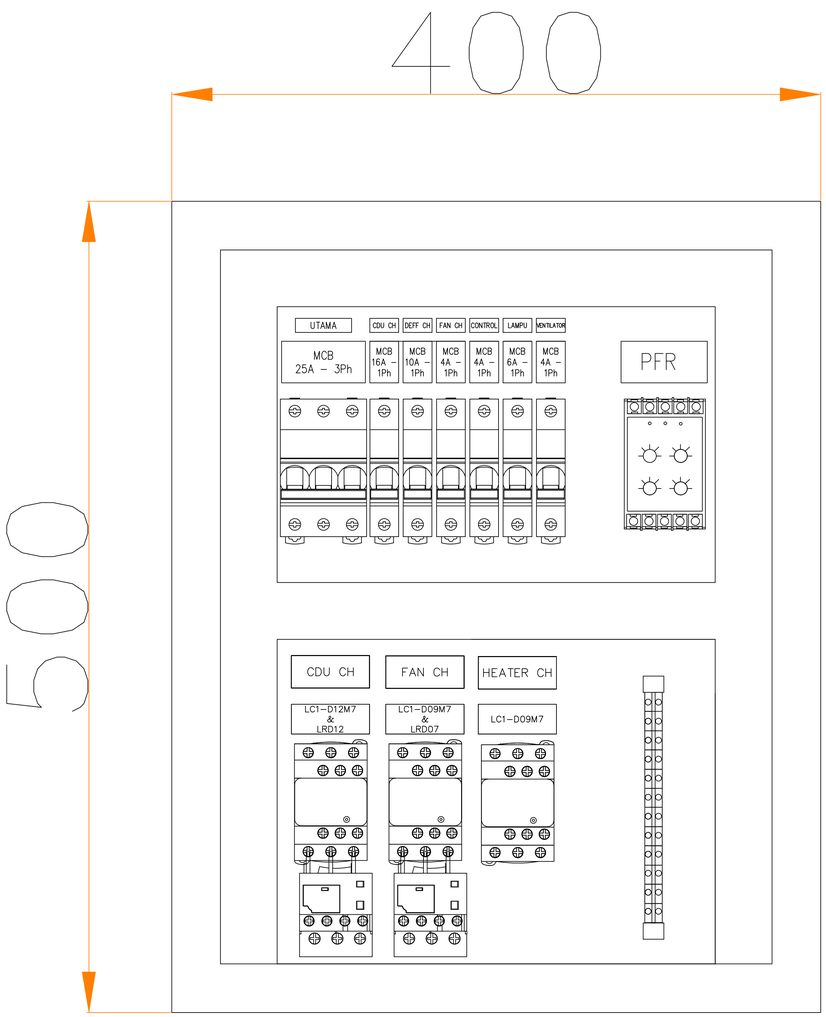

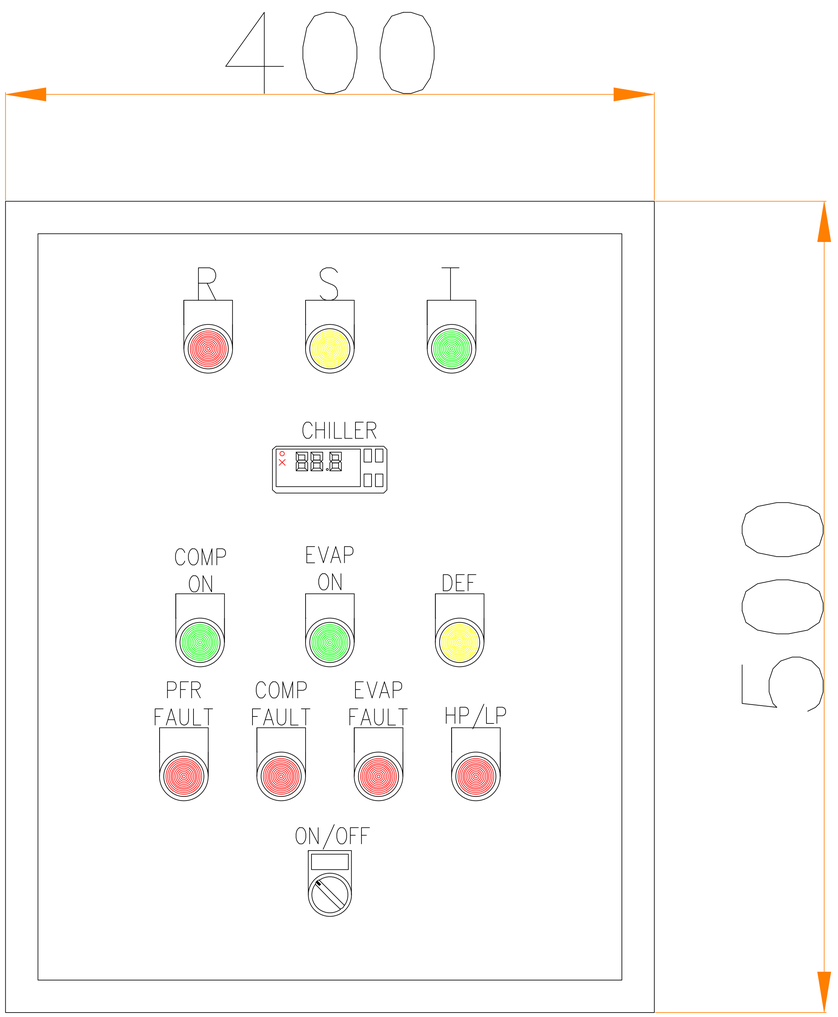

REV	DESCRIPTION	DATE	DRAWN	CHECKED	APPROVED
	FOR APPROVAL	15 - 09 - 2026	RY	RB	

ROKINDO JAYA MANDIRI
Green Lake City, Rukan Fresh Market Blok B No.12 & 18
Cipondoh, Tangerang Tel: 021-5503476

PROJECT	LION SUPER INDO	PANEL NAME	CONTROL PANEL
		DWG TITLE	CHILLER PANEL
LOKASI	CITRA GARDEN SERPONG	DWG NO.	-

QUANTITY	-
SCALE	NTS
SHEET NO.	15
TOTAL SHEET	15